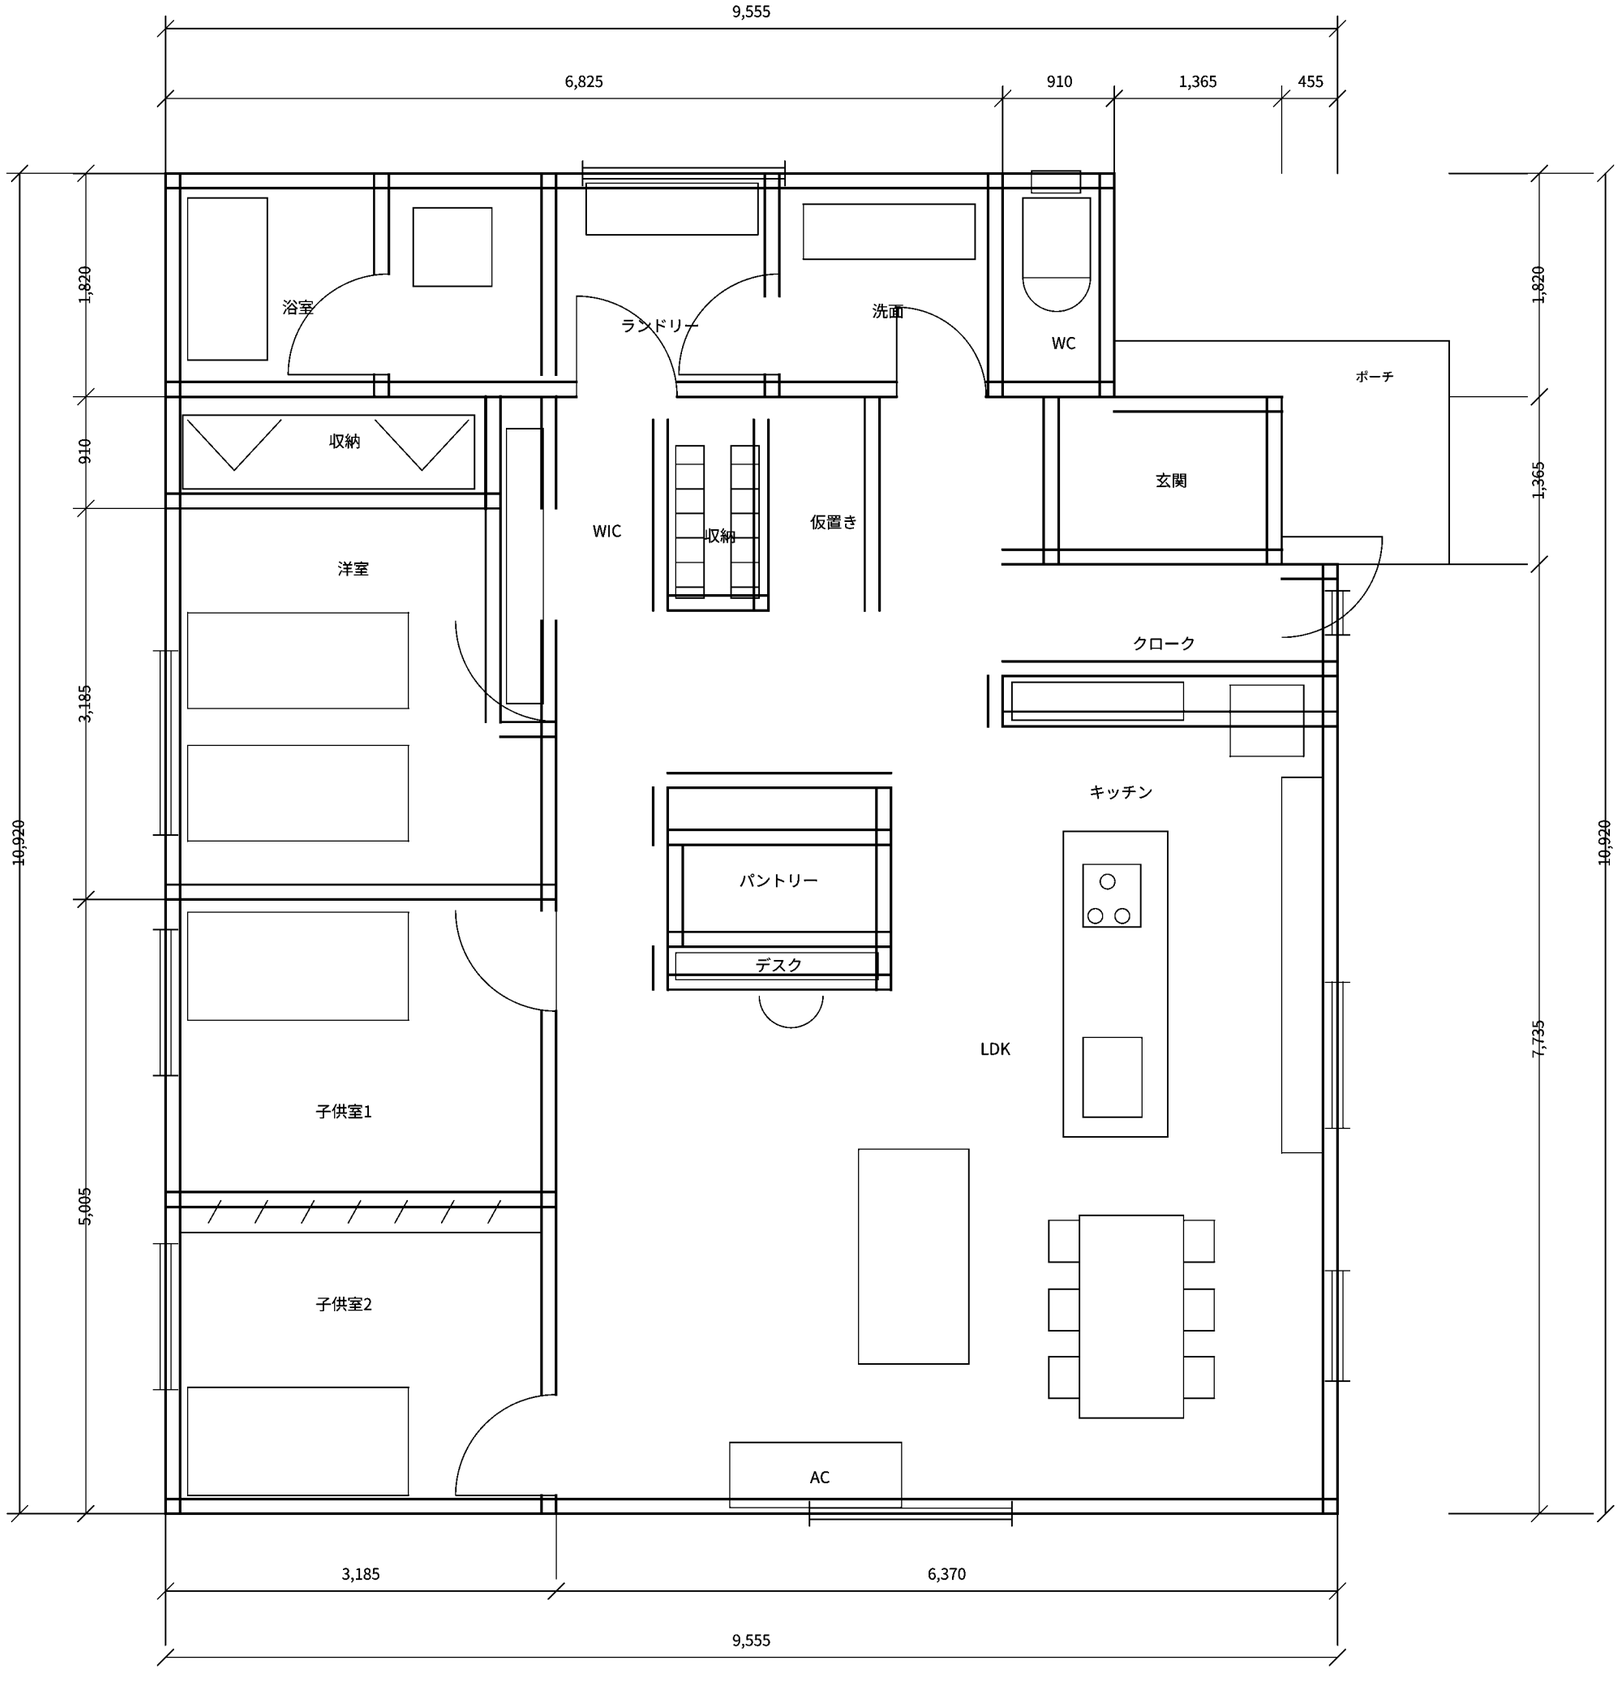

画像からの参考作図

A3 / 縮尺 1:50

寸法単位：mm

外形：9,555 × 10,920

室内配置・壁厚・開口は推定

ポーチ位置・幅は推定

手書き寸法の不明箇所は未反映

面積数値は検証できず未記載

施工・確認申請には使用不可

現地実測・原図照合が必要

線・文字・円弧は編集可能 / 未確定箇所は原図確認後に修正